경산 진량 단독주택 신축공사

인허가·실시설계 도서 (초안) | 경일대학교 건축학부 건축설계



건축개요

구분	내용
대지위치	경상북도 경산시 진량읍 신제리·다문리 일원
	경산4일반산업단지 단독주택용지 (필지 미정)
지역·지구	제1종일반주거지역, 지구단위계획구역
용도 / 구조	단독주택 / 철근콘크리트 벽식구조, 박공지붕
대지면적	290.00㎡
건축면적	82.39㎡
연면적	149.38㎡ (1층 82.39 / 2층 66.99)
건폐율 / 용적률	28.41% / 51.51%
규모 / 높이	지상 2층 / 8.68 m (층고 3.0 m)
주차 / 조경	2대 / 87.90㎡
단열 (U, W/㎡K)	외벽 0.188 / 지붕 0.120 / 바닥 0.195

도면 목록

번호	도면명	축척
A-000	표지·건축개요·법규검토	-
A-001	면적표·창호일람표·마감표	-
A-101	배치도	1/200
A-201	1층 평면도	1/50
A-202	2층 평면도	1/50
A-203	지붕 평면도	1/50
A-301	남측·북측 입면도	1/100
A-302	동측·서측 입면도	1/100
A-401	단면도 A-A'	1/50
A-402	단면도 B-B'	1/50
A-501	상세 1·2 (기초, 2층 바닥)	1/20
A-502	상세 3·4 (처마, 테라스)	1/20
S-001	구조 일반사항·부재일람표	-
S-101	구조 평면도	1/100

법규 검토

항목	계획	기준	판정
건폐율	82.39 / 290 = 28.41%	60% 이하	적합
용적률	149.38 / 290 = 51.51%	180% 이하	적합
층수·높이	지상 2층, 최고높이 8.68 m	3층 이하	적합
정북 일조	정북 인접대지경계선에서 3.0 m	높이 10 m 이하 부분 1.5 m 이상	적합
접도	폭 6 m 도로에 14.5 m 접함	4 m 이상 도로에 2 m 이상	적합
주차	2대 (2.5 x 5.0 m 일반형)	1대 이상	적합
조경	87.9 ㎡ (30%)	경산시 건축조례 기준	적합
계단	단높이 176.5 / 단너비 260 / 너비 1000 mm	200 이하 / 240 이상 / 600 이상	적합
난간	테라스·계단 개구부 1200 mm	1,200 mm 이상	적합
인접 이격	서 1.5 m, 동 2.0 m, 북 3.0 m, 남 9.0 m	0.5 m 이상	적합
처마	내밀기 0.5 m	1 m 미만 → 건축면적 불산입	적합
내진	지상 2층 → 구조안전 확인 대상	내진설계 적용	적합
허용용도	단독주택 (다중주택 아님)	단독주택·점포주택	적합
건축한계선	전면 도로 6 m (소로), 도로 이격 9.0 m	대로 2 m / 중로 1 m	적합
담장	생울타리 H1,200	1.2 m 이하 투시형 또는 생울타리	적합
옥상 설비	실외기 지상 설치, 지붕 위 설비 없음	도로에서 보이지 않게	적합

대지 290.00 ㎡ · 건축면적 82.39 ㎡ · 연면적 149.38 ㎡ (1층 82.39, 2층 66.99) · 층고 3.0 m

PROJECT TITLE

경산 진량 단독주택 신축공사

PROJECT NO.

건축설계

NOTE

도서 구성
A3 양식 출력 기준 축척입니다.
평면·단면·지붕 1/50, 입면 1/100, 배치 1/200, 상세 1/20.

기준 확인
용도지역 기준값은 공개 자료 기준이며 해당 필지의 지구단위계획 결정도서로 확인이 필요합니다.

주의
인허가·실시설계 검토용 초안입니다.
건축사·구조기술사의 검토와 날인 전에는 시공·제출에 쓰지 않습니다.
치수 mm, 레벨 기준 GL±0 (설계 지반고).

NO.	DATE	DRAWN	REVISION NOTE
△			
△			
△			

경일대학교 건축학부
Kyungil University School of Architecture

ARCHITECT 건축사
APPROVED BY 승인
CHECKED BY 검토
DRAWN BY 도면작성 연제욱 (20202672)

DATE 작성일자 2026. 11.

DRAWING TITLE 도면작성

표지·건축개요

SCALE NONE

DRAWING NO. **A-000**

면적표

층	바닥면적(㎡)	용도
1층	82.39	단독주택
2층	66.99	단독주택
합계	149.38	

층	실명	면적(㎡)
1층	거실	21.09
1층	주방·식당	21.09
1층	화장실	5.06
1층	현관	4.62
1층	홀	10.18
1층	다용도실	5.52
1층	계단실	6.47
2층	안방	15.91
2층	드레스룸	5.01
2층	욕실	5.46
2층	방2	14.10
2층	홀	11.95
2층	테라스	14.25

창호일람표

기호	층	위치	규격 W x H	하단	형식·사양
W1	1F	거실	4,500 x 2,200	FL+100	PVC 시스템 슬라이딩도어, 43mm 삼중 로이유리
W2	1F	화장실	1,000 x 600	FL+1,500	PVC 시스템창호, 24mm 삼중 로이유리 (불투명)
D1	1F	현관	1,000 x 2,100	FL+0	단열 현관문 (방화·방범), 열관류율 1.4 이하
W3	1F	주방	2,400 x 1,100	FL+1,000	PVC 시스템창호, 24mm 삼중 로이유리
W4	1F	다용도실	1,000 x 900	FL+1,200	PVC 시스템창호, 24mm 삼중 로이유리
W5	1F	거실	2,500 x 1,300	FL+900	PVC 시스템창호, 24mm 삼중 로이유리
W6	1F	식당	2,000 x 1,300	FL+900	PVC 시스템창호, 24mm 삼중 로이유리
W7	1F	계단실	1,400 x 600	FL+2,000	PVC 시스템창호, 24mm 삼중 로이유리
W8	2F	안방	2,600 x 1,300	FL+900	PVC 시스템창호, 24mm 삼중 로이유리
W9	2F	방2	3,000 x 1,300	FL+900	PVC 시스템창호, 24mm 삼중 로이유리
W10	2F	욕실	1,000 x 600	FL+1,500	PVC 시스템창호, 24mm 삼중 로이유리 (불투명)
W11	2F	홀	1,800 x 1,200	FL+900	PVC 시스템창호, 24mm 삼중 로이유리
D2	2F	안방	900 x 2,100	FL+0	PVC 시스템 여닫이문, 24mm 삼중 로이유리
W12	2F	안방	1,600 x 1,300	FL+900	PVC 시스템창호, 24mm 삼중 로이유리
W13	2F	방2	1,800 x 1,300	FL+900	PVC 시스템창호, 24mm 삼중 로이유리
AD1	1·2F	3개소	900 x 2,100	FL	ABS 도어 + 목재 문틀
AD2	1·2F	4개소	800 x 2,100	FL	ABS 도어 (욕실·다용도: 방수형)
AD3	1·2F	1개소	900 x 2,100	FL	현관 중문 (강화유리 + 알루미늄 프레임)

실내재료마감표

층	실명	바닥	걸레받이	벽	천장	반자
1F	거실	강마루 THK10	PVC 걸레받이 H80	실크벽지	석고보드 9.5 2겹 위 수성페인트	2,400
1F	주방·식당	강마루 THK10	PVC 걸레받이 H80	실크벽지	석고보드 9.5 2겹 위 수성페인트	2,400
1F	화장실	포세린타일 300x300 (논슬립)	-	포세린타일 300x600	SMC 천장재	2,400
1F	현관	포세린타일 600x600	타일 걸레받이 H100	실크벽지	석고보드 9.5 2겹 위 수성페인트	2,400
1F	홀	강마루 THK10	PVC 걸레받이 H80	실크벽지	석고보드 9.5 2겹 위 수성페인트	2,400
1F	다용도실	포세린타일 300x300	타일 걸레받이 H100	수성페인트	석고보드 9.5 2겹 위 수성페인트	2,400
1F	계단실	강마루 계단재	-	실크벽지	석고보드 위 수성페인트	2,400
2F	안방	강마루 THK10	PVC 걸레받이 H80	실크벽지	석고보드 9.5 2겹 위 수성페인트	2,400
2F	드레스룸	강마루 THK10	PVC 걸레받이 H80	실크벽지	석고보드 9.5 2겹 위 수성페인트	2,400
2F	욕실	포세린타일 300x300 (논슬립)	-	포세린타일 300x600	SMC 천장재	2,400
2F	방2	강마루 THK10	PVC 걸레받이 H80	실크벽지	석고보드 9.5 2겹 위 수성페인트	2,400
2F	홀	강마루 THK10	PVC 걸레받이 H80	실크벽지	석고보드 9.5 2겹 위 수성페인트	2,400
2F	테라스	합성목재 데크 (우레탄 도막방수 위)	-	스터코 (외벽)	-	-

PROJECT TITLE

경산 진량 단독주택 신축공사

PROJECT NO.

건축설계

NOTE

면적 산정
바닥면적: 외벽 중심선 (외단열 포함 벽두께의 중심, 건축법 시행령 제119조)
실면적: 마감면 기준 안목치수

창호
PVC 시스템창호, 24mm 삼중 로이유리, 단열간봉
현관문: 단열 방화·방범문

주의
인허가·실시설계 검토용 초안입니다.
건축사·구조기술사의 검토와 날인 전에는 시공·제출에 쓰지 않습니다.
치수 mm, 레벨 기준 GL±0 (설계 지반고).

NO.	DATE	DRAWN	REVISION NOTE
△			
△			
△			

경일대학교
건축학부
Kyungil University
School of Architecture

ARCHITECT 건축사

APPROVED BY 승인

CHECKED BY 검토

DRAWN BY 도면작성
연제욱 (20202672)


DATE 작성일자
2026. 11.

DRAWING TITLE 도면작성
면적표·창호·마감표

SCALE
NONE

DRAWING NO.
A-001

항목	내용
대지위치	경북 경산시 진량읍 신제리·다문리 일원
	경산4일반산업단지 단독주택용지 (필지 미정)
지역·지구	제1종일반주거지역, 지구단위계획구역
대지면적	290.00㎡ (14,500 x 20,000)
건축면적	82.39㎡ (건폐율 28.41%)
연면적	149.38㎡ (용적률 51.51%)
규모·높이	지상 2층, 최고높이 8.68m
주차	2대 (법정 1대), 2.5 x 5.0 m
조경	87.90㎡ (30.3%)
이격거리	정북 3.0 / 서 1.5 / 동 2.0 / 남 9.0 m

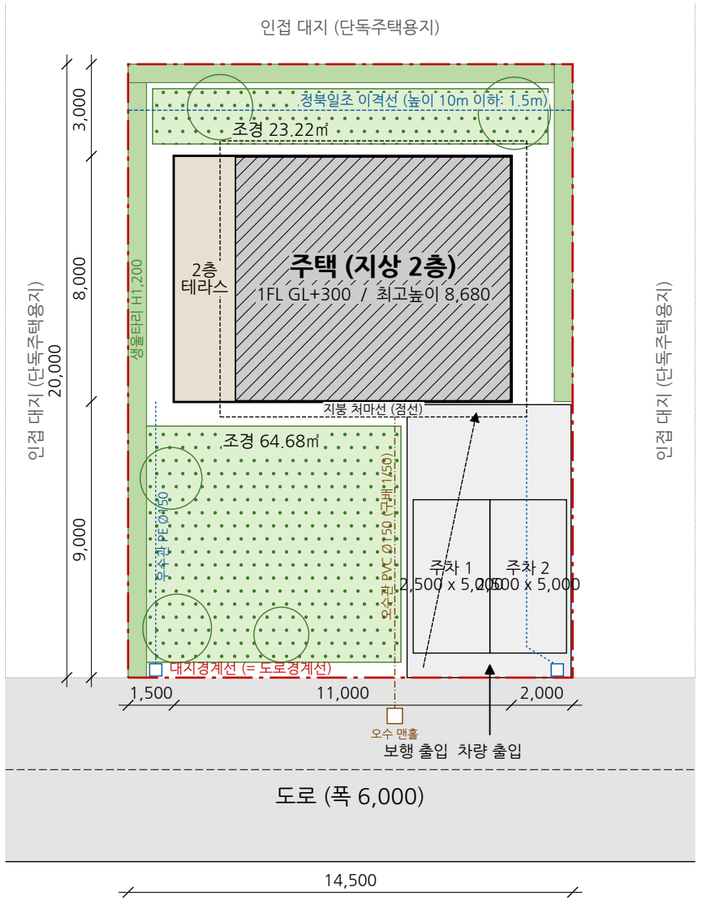

배치도

SCALE 1/200

PROJECT TITLE

경산 진량 단독주택 신축공사

PROJECT NO.

건축설계

NOTE

배치 사항

필지 확정 후 지적측량 성과도로 대지 형상·면적·도로 폭을 다시 확인합니다.

설계 지반고 GL±0 = 도로 경계 보도 상단 +150 (현황측량 후 확정).

설비 인입

오수: 분류식 공공하수관 직접 연결 (정화조 없음).

우수: 선홈통 → 우수관 PE Ø150 → 도로측 우수 맨홀.

외부

생울타리 H1,200 (서·북·동), 주차 2대 일반형.

주의

인허가·실시설계 검토용 초안입니다.
건축사·구조기술사의 검토와 날인 전에는 시공·제출에 쓰지 않습니다.
치수 mm, 레벨 기준 GL±0 (설계 지반고).

NO.	DATE	REVISION NOTE
△		
△		
△		

경일대학교
건축학부
Kyungil University
School of Architecture

ARCHITECT 건축사

APPROVED BY 승인

CHECKED BY 검토


DRAWN BY 도면작성: 연제욱 (20202672)

DATE 작성일자: 2026. 11.

DRAWING TITLE 도면작성: **배치도**

SCALE: 1/200

DRAWING NO.: **A-101**

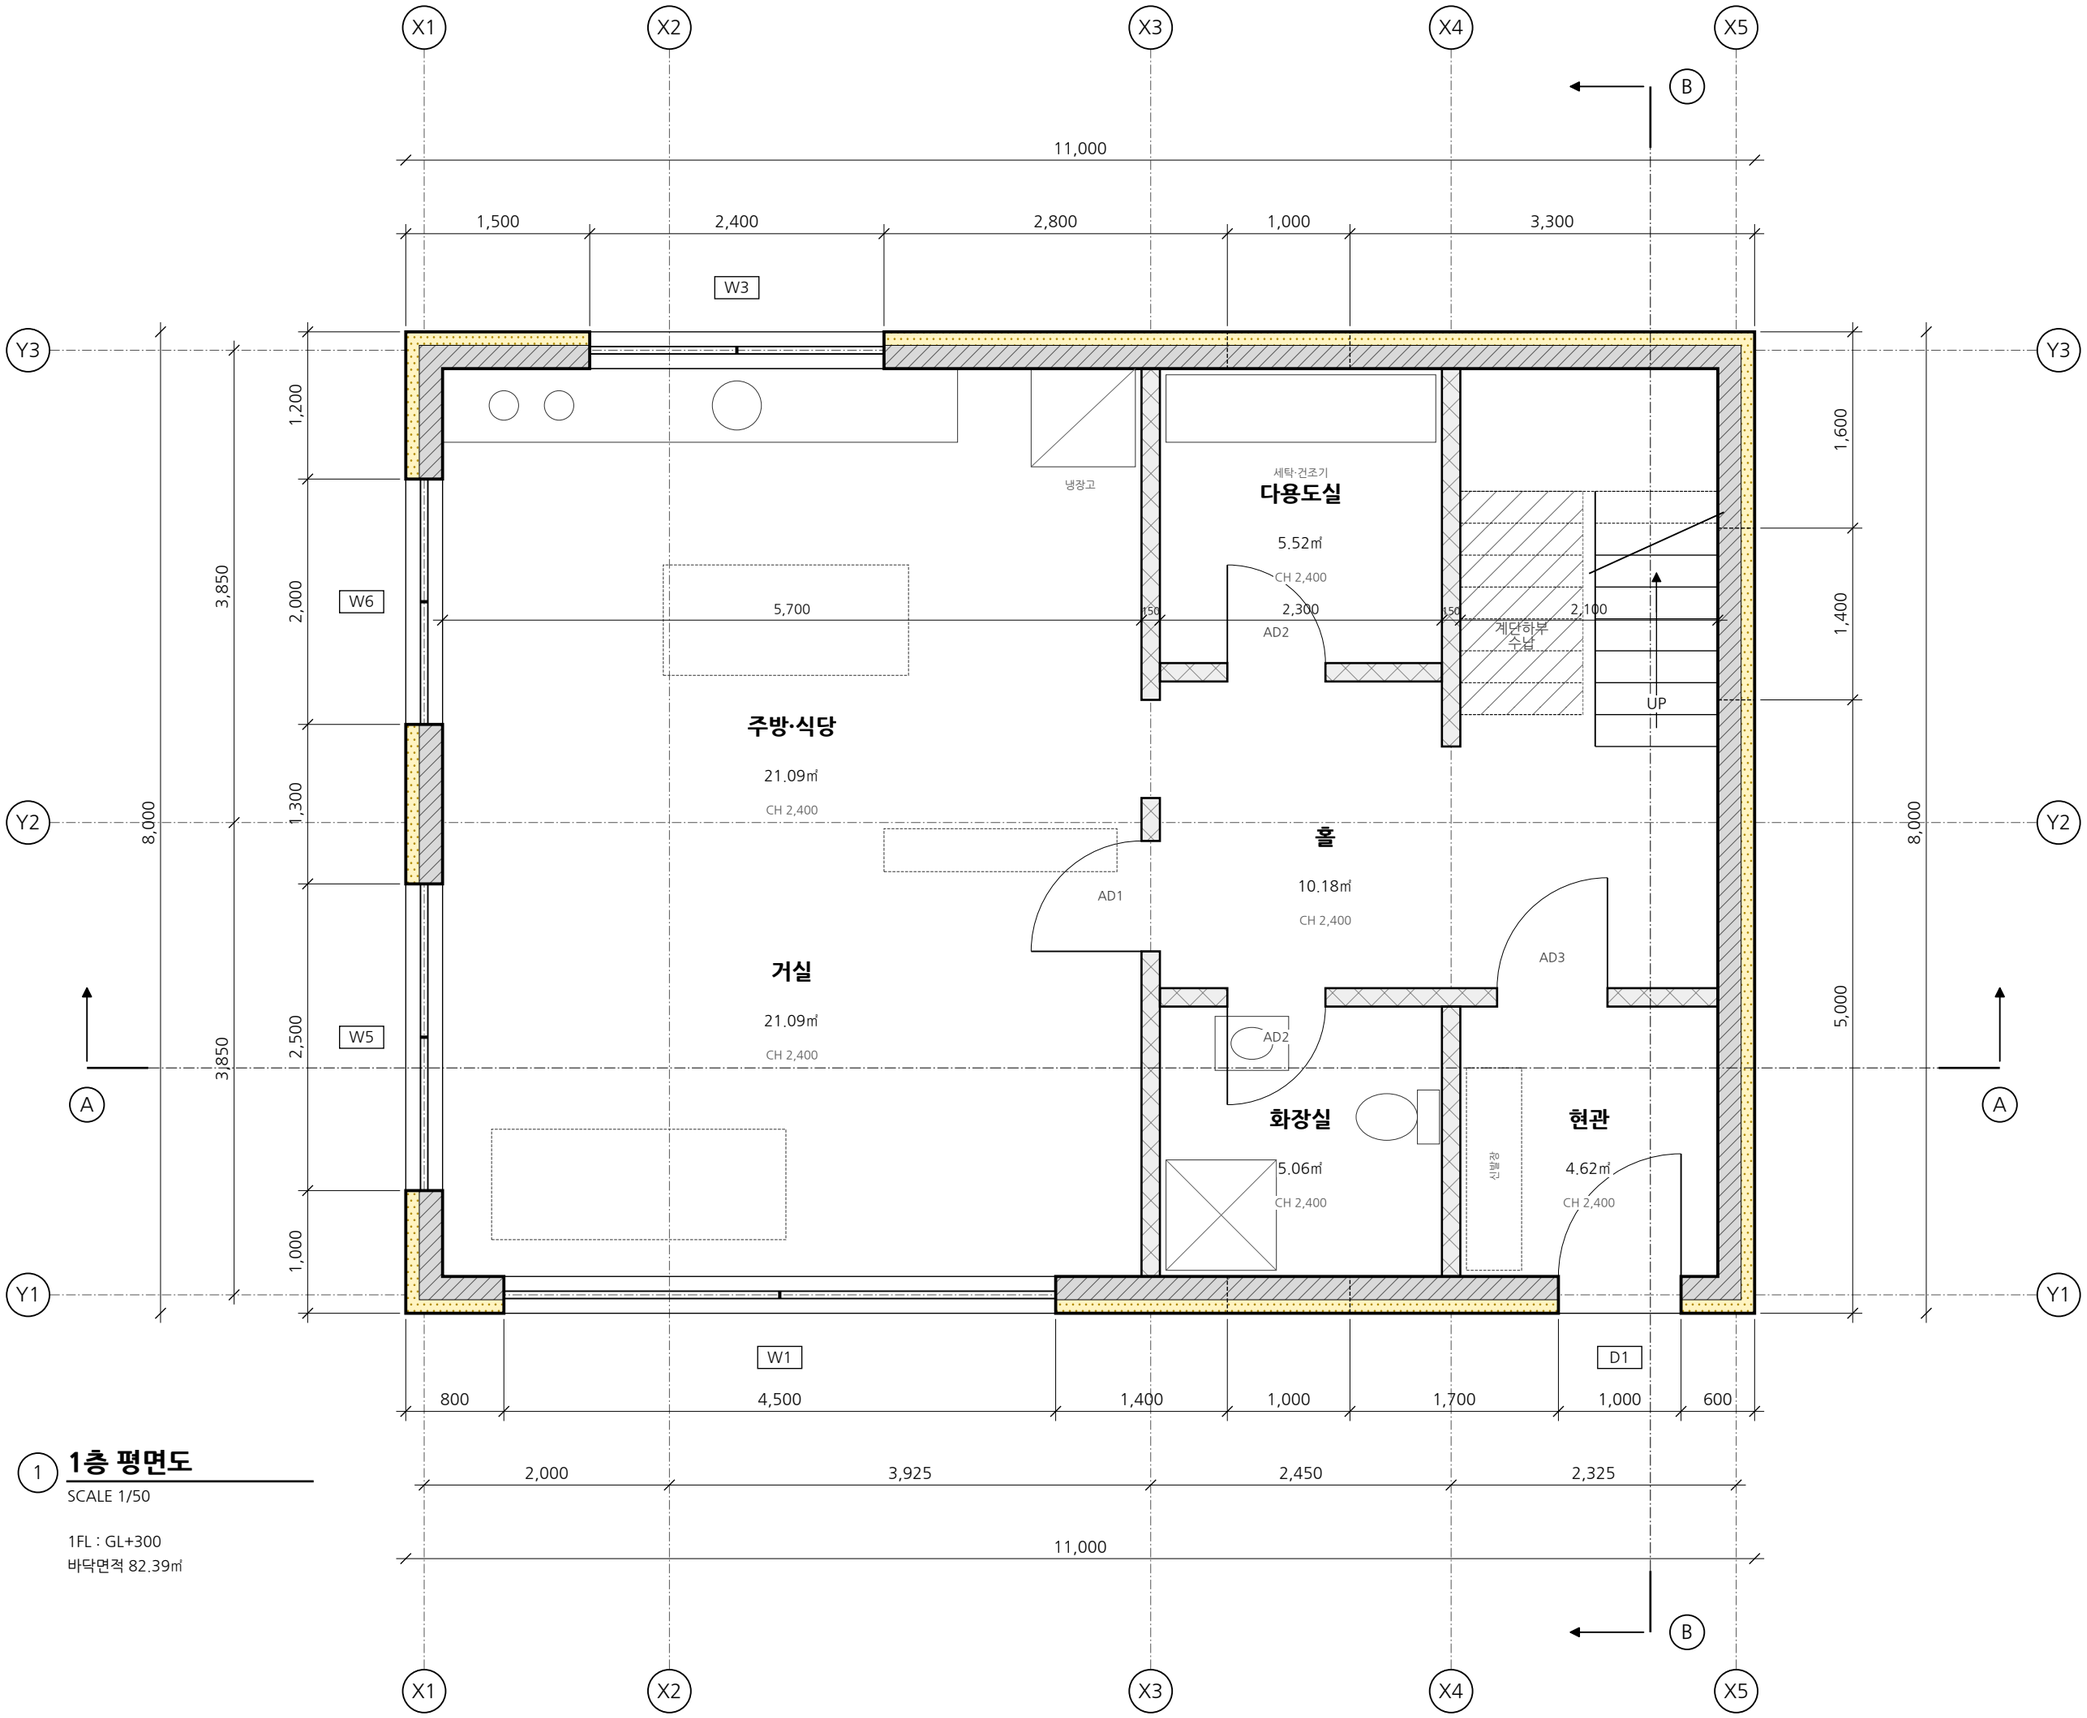

① 1층 평면도

SCALE 1/50

1FL : GL+300
바닥면적 82.39㎡

PROJECT TITLE

경산 진량 단독주택 신축공사

PROJECT NO.

건축설계

NOTE

일반 사항

1. 외벽: 스터코 10 + PF보드(준불연) 100 + RC 180 + 석고보드 9.5 (총 300)
2. 내벽: 경량철골 칸막이 + 석고보드 9.5 2겹 양면 (THK150), 욕실·다용도실은 방수석고보드
3. 창호 기호 W·D: A-001 창호일람표, AD: 내부 문
4. 절단 높이 FL+1,200 위의 창은 점선
5. 단면 표시 A-A' (A-401), B-B' (A-402)
6. 치수: 외벽 바깥면·그리드(벽 중심선) 기준
7. 현관 바닥 FL-30, 화장실 FL-20 (구배 1/100)
8. 계단 하부 수납장 (점검구 600x600)

철근콘크리트

외단열 PF보드

경량 칸막이

주의
인허가·실시설계 검토용 초안입니다.
건축사·구조기술사의 검토와 날인 전에는 시공·제출에 쓰지 않습니다.
치수 mm, 레벨 기준 GL±0 (설계 지반고).

NO.	DATE	REVISION NOTE
	DRAWN	

경일대학교
건축학부
Kyungil University
School of Architecture

ARCHITECT 건축사

APPROVED BY 승인

CHECKED BY 검토


DRAWN BY 도면작성: 연제욱 (20202672)

DATE 작성일자: 2026. 11.

DRAWING TITLE 도면작성: **1층 평면도**

SCALE: 1/50

DRAWING NO.: **A-201**

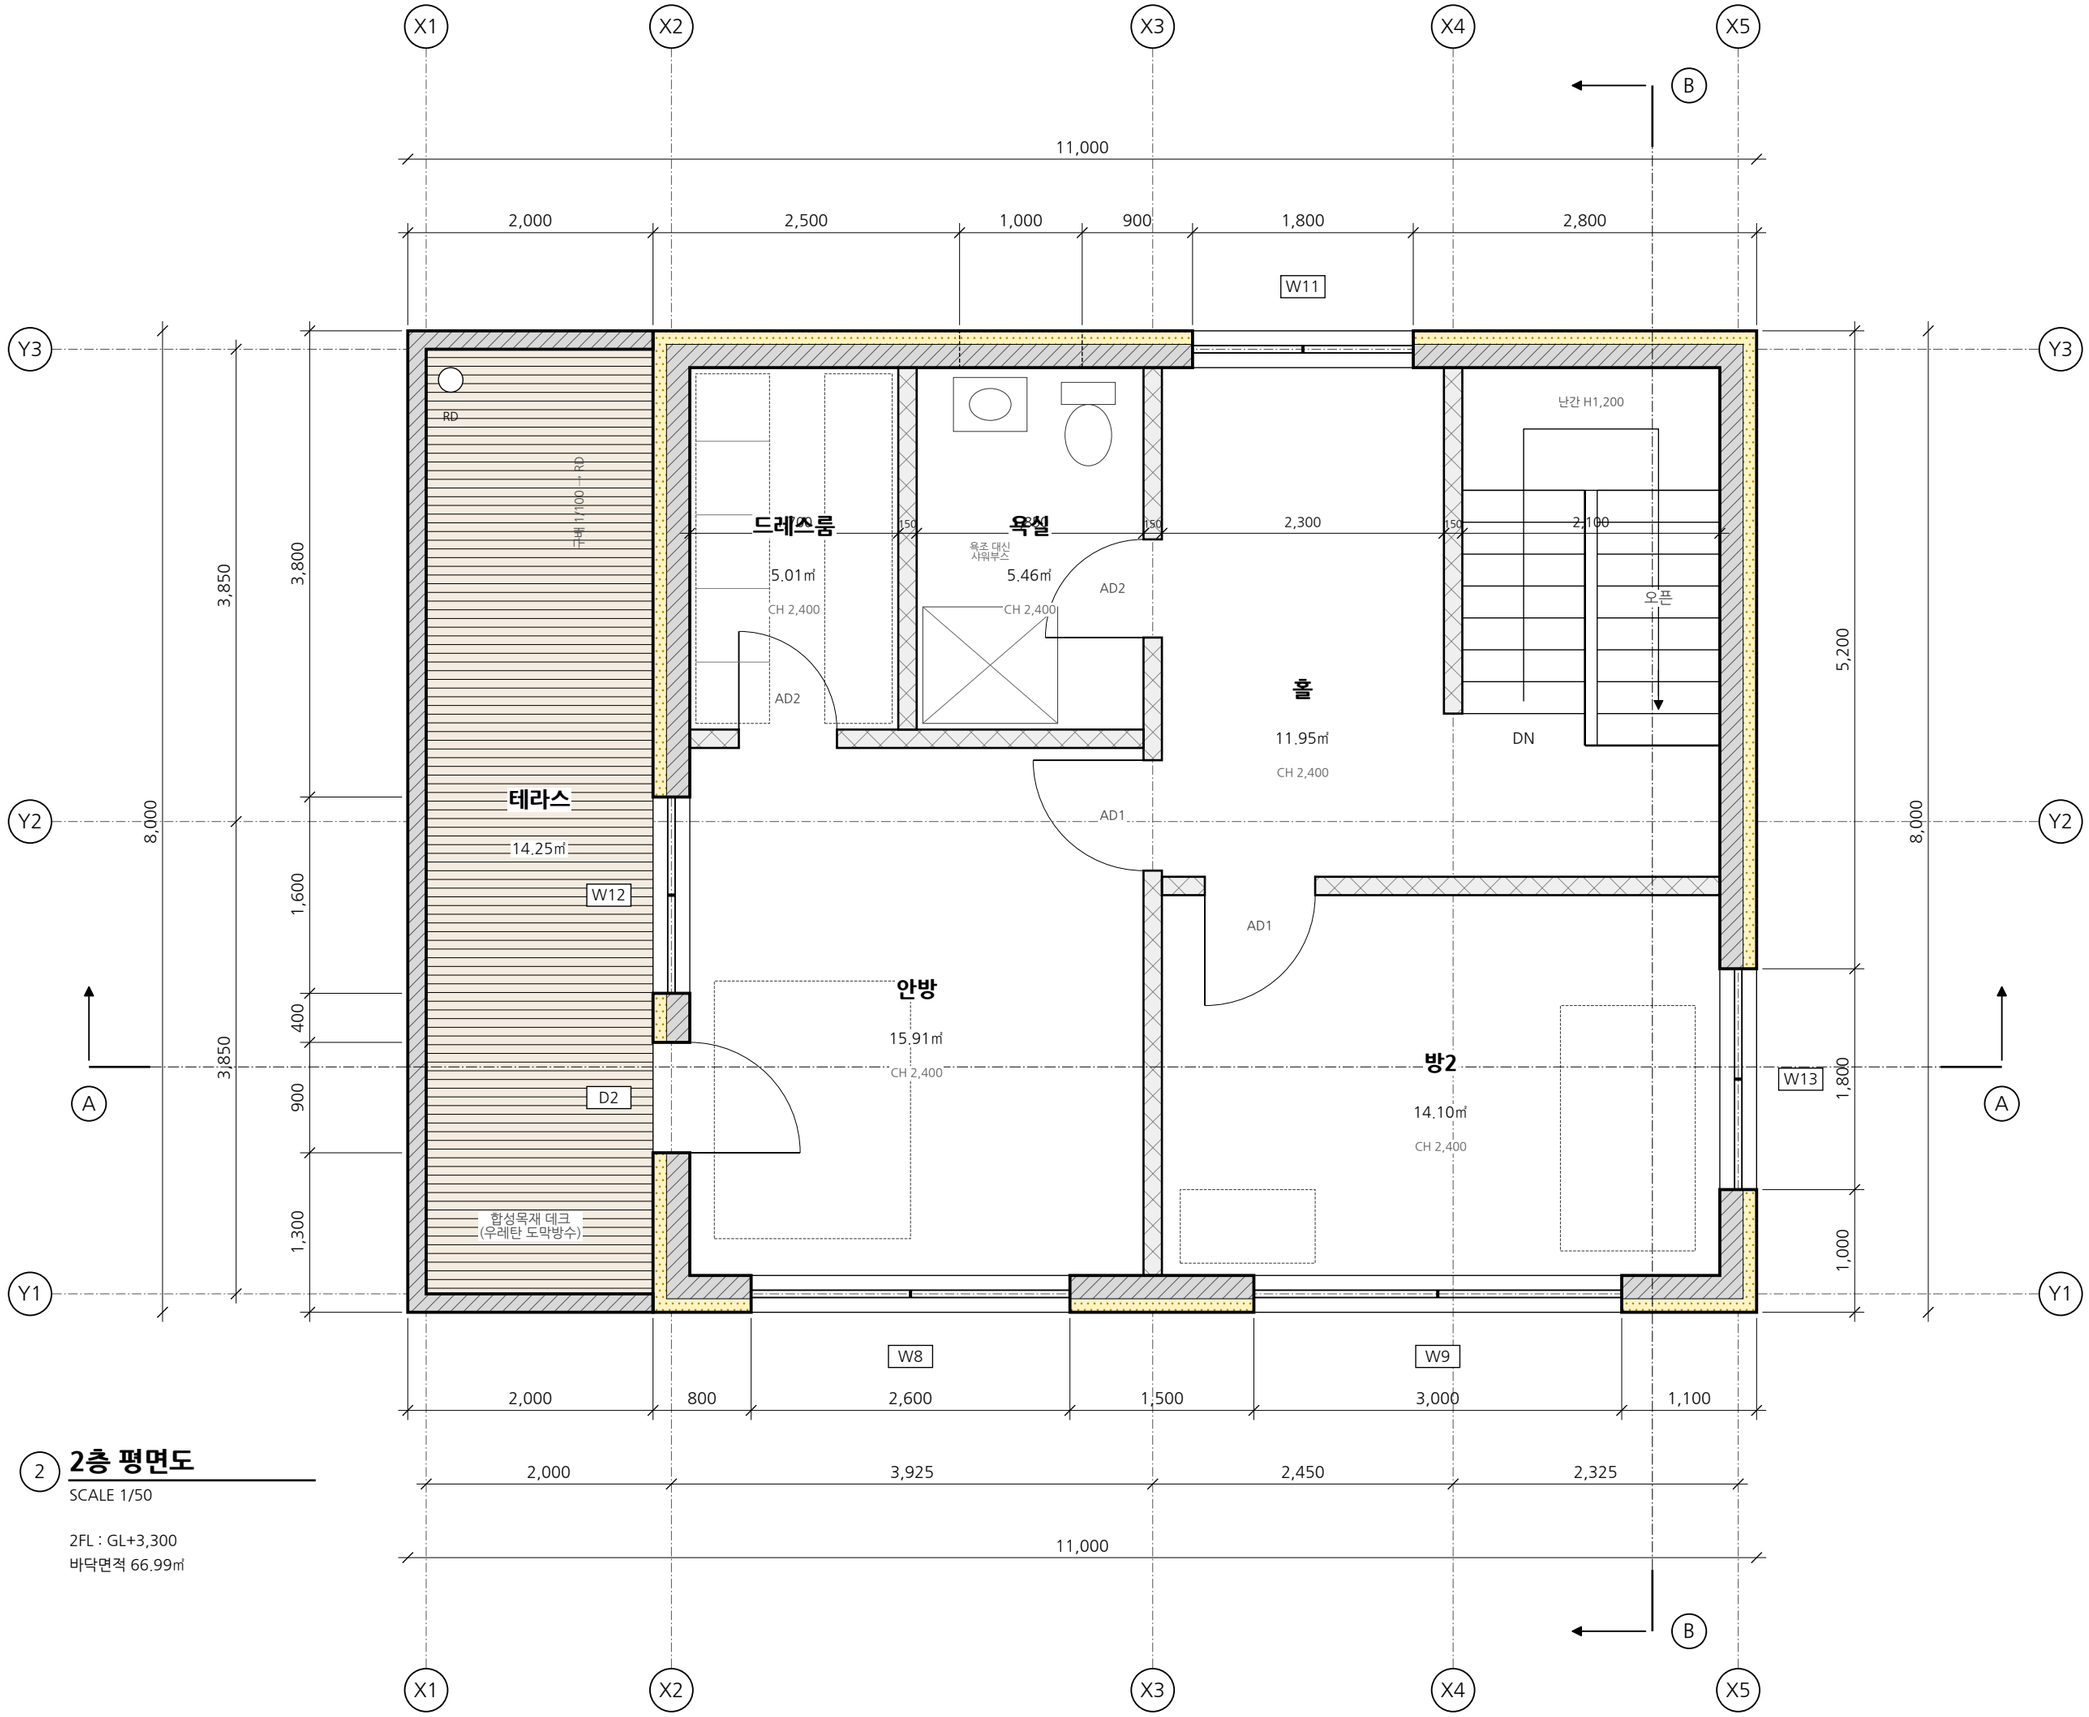

2 2층 평면도

SCALE 1/50

2FL : GL+3,300
바닥면적 66.99㎡

PROJECT TITLE

경산 진량 단독주택 신축공사

PROJECT NO.

건축설계

NOTE

일반 사항

1. 외벽: 스터코 10 + PF보드(준불연) 100 + RC 180 + 석고보드 9.5 (총 300)
2. 내벽: 경량철골 칸막이 + 석고보드 9.5 2겹 양면 (THK150), 욕실·다용도실은 방수석고보드
3. 창호 기호 W·D: A-001 창호일람표, AD: 내부 문
4. 절단 높이 FL+1,200 위의 창은 점선
5. 단면 표시 A-A' (A-401), B-B' (A-402)
6. 치수: 외벽 바깥면·그리드(벽 중심선) 기준
7. 계단 오픈부 난간 H1,200 (강관 + 강화유리)
8. 테라스: 우레탄 도막방수, RD 루프드레인 Ø100, 파라펫 H1,200, 데크 +3,250

철근콘크리트

외단열 PF보드

경량 칸막이

주의
인허가·실시설계 검토용 초안입니다.
건축사·구조기술사의 검토와 날인 전에는 시공·제출에 쓰지 않습니다.
치수 mm, 레벨 기준 GL±0 (설계 지반고).

NO.	DATE	REVISION NOTE
	DRAWN	

경일대학교 건축학부
Kyungil University
School of Architecture

ARCHITECT 건축사

APPROVED BY 승인

CHECKED BY 검토


DRAWN BY 도면작성: 연제욱 (20202672)

DATE 작성일자: 2026. 11.

DRAWING TITLE 도면작성: **2층 평면도**

SCALE: 1/50

DRAWING NO.: **A-202**

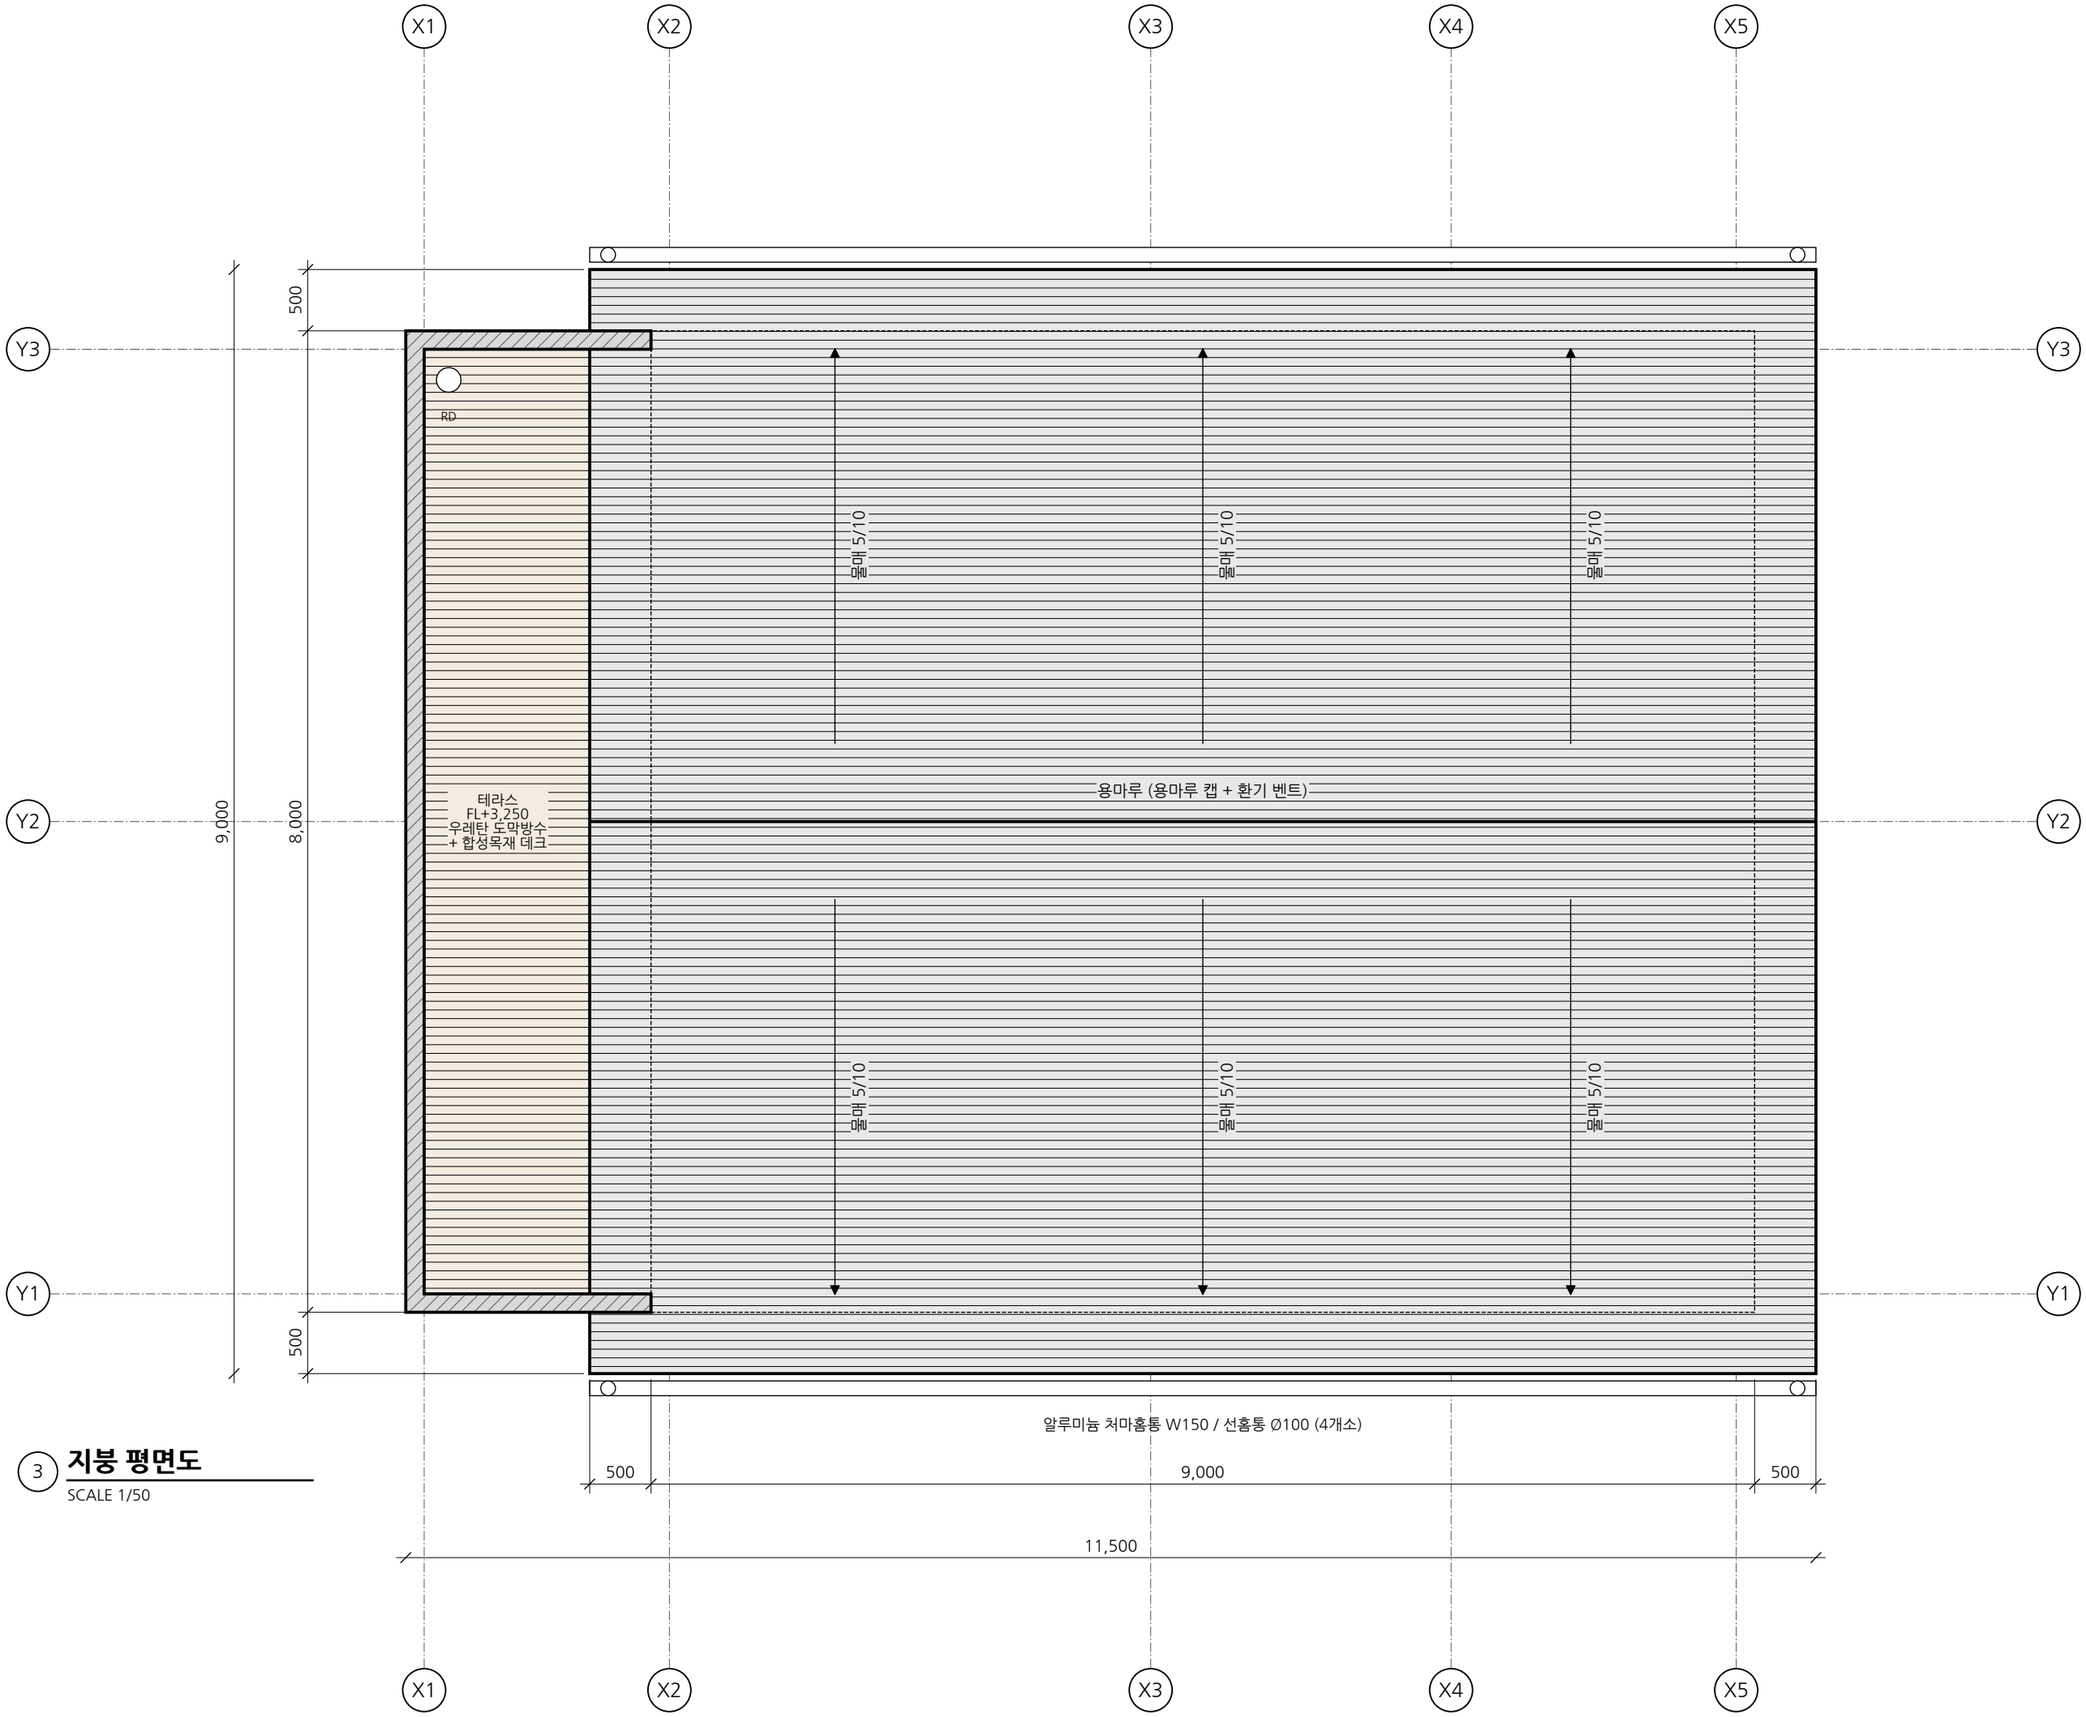

3 지붕 평면도

SCALE 1/50

PROJECT TITLE

경산 진량 단독주택 신축공사

PROJECT NO.

건축설계

NOTE

일반 사항

1. 지붕: 아스팔트 싱글 / 자착식 방수시트 / OSB 11 / 통기층 30 / PF보드 160 / RC 150
2. 처마 하부 펀칭 소핏 → 용마루 벤트로 통기
3. 처마홈통·선홈통: 알루미늄, 선홈통은 우수 맨홀로 연결
4. 테라스 RD: 루프드레인 Ø100 + 오버플로 1개소
5. 박공 끝 (동·서): 알루미늄 후레싱
6. 처마 내밀기 500 (1 m 미만, 건축면적 불산입)

주의

인허가·실시설계 검토용 초안입니다.
건축사·구조기술사의 검토와 날인 전에는 시공·제출에 쓰지 않습니다.
치수 mm, 레벨 기준 GL±0 (설계 지반고).

NO.	DATE / DRAWN	REVISION NOTE
△		
△		
△		

경일대학교
건축학부
Kyungil University
School of Architecture

ARCHITECT 건축사

APPROVED BY 승인

CHECKED BY 검토


DRAWN BY 도면작성: 연제욱 (20202672)

DATE 작성일자: 2026. 11.

DRAWING TITLE 도면작성: **지붕 평면도**


SCALE: 1/50

DRAWING NO.: **A-203**

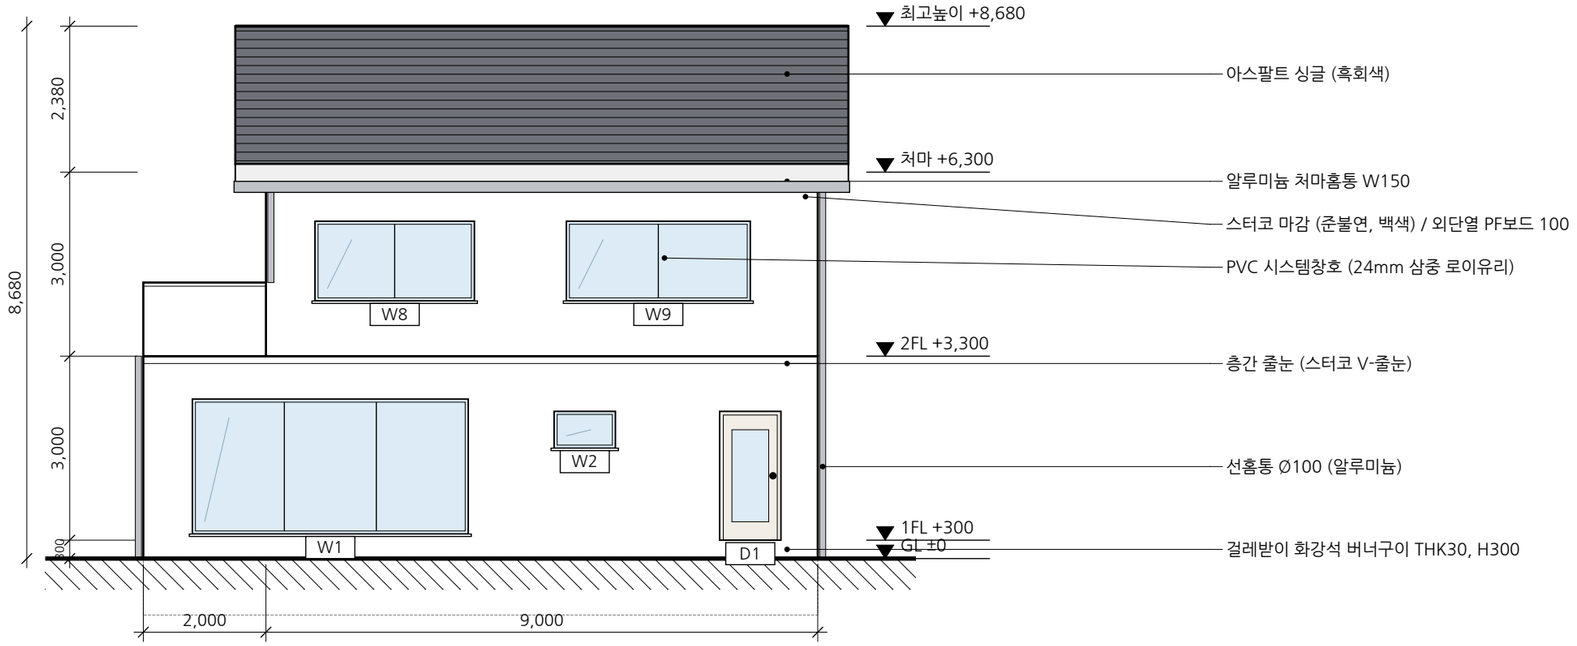

① 남측 입면도

SCALE 1/100

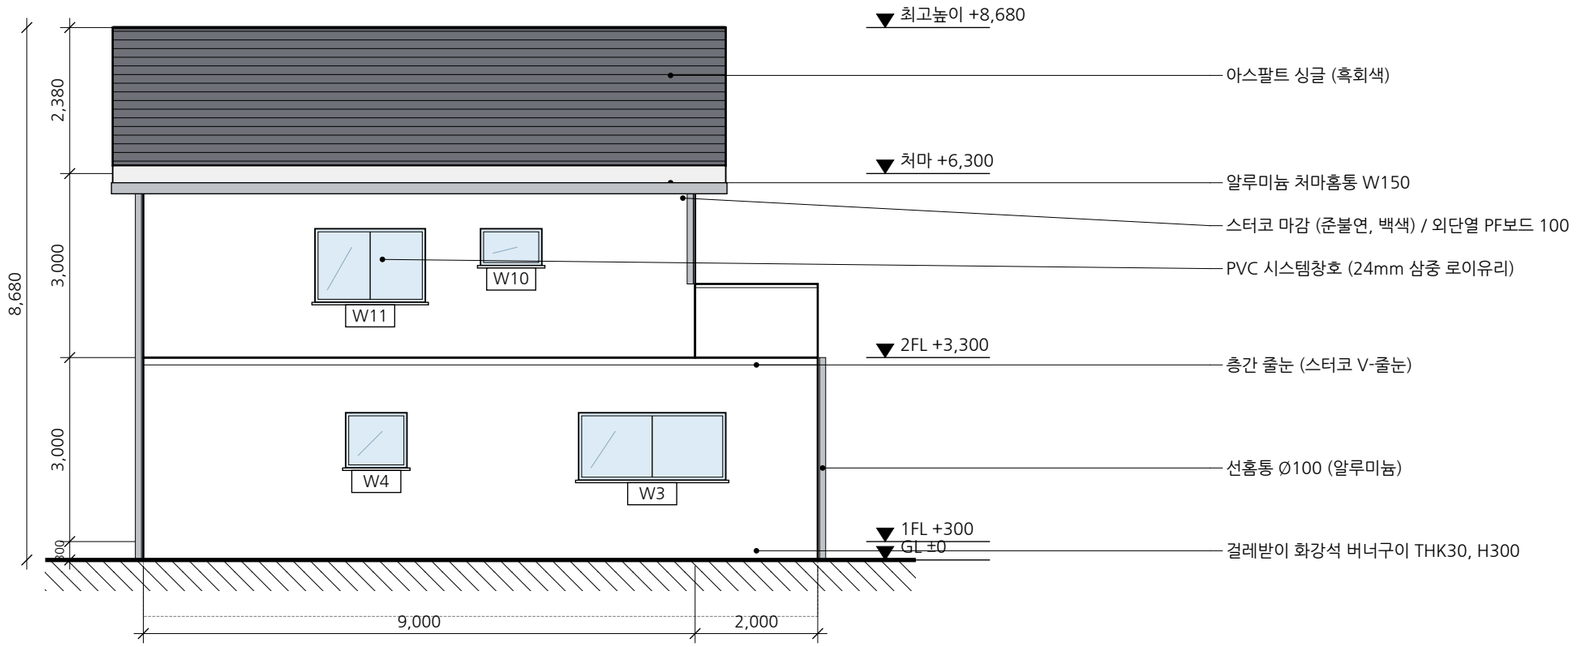

② 북측 입면도

SCALE 1/100

PROJECT TITLE

경산 진량 단독주택 신축공사

PROJECT NO.

건축설계

NOTE

외부 마감

1. 외벽: 스터코(준불연) 백색, 걸레받이 화강석 THK30 H300
2. 지붕: 아스팔트 싱글 (흑회색), 처마 하부 알루미늄 소핏
3. 창호: PVC 시스템창호 (회색), 삼중 로이유리
4. 홈통: 알루미늄 처마홈통 W150, 선홈통 Ø100
5. 테라스 파라펫: RC + 외단열, 알루미늄 두겁

주의

인허가·실시설계 검토용 초안입니다.
건축사·구조기술사의 검토와 날인 전에는 시공·제출에 쓰지 않습니다.
치수 mm, 레벨 기준 GL±0 (설계 지반고).

NO.	DATE / DRAWN	REVISION NOTE
△		
△		
△		

경일대학교
건축학부
Kyungil University
School of Architecture

ARCHITECT 건축사

APPROVED BY 승인

CHECKED BY 검토

DRAWN BY 도면작성: 연제욱 (20202672)


DATE 작성일자: 2026. 11.

DRAWING TITLE 도면작성

남측 입면도 · 북측 입면도


SCALE: 1/100

DRAWING NO.: **A-301**

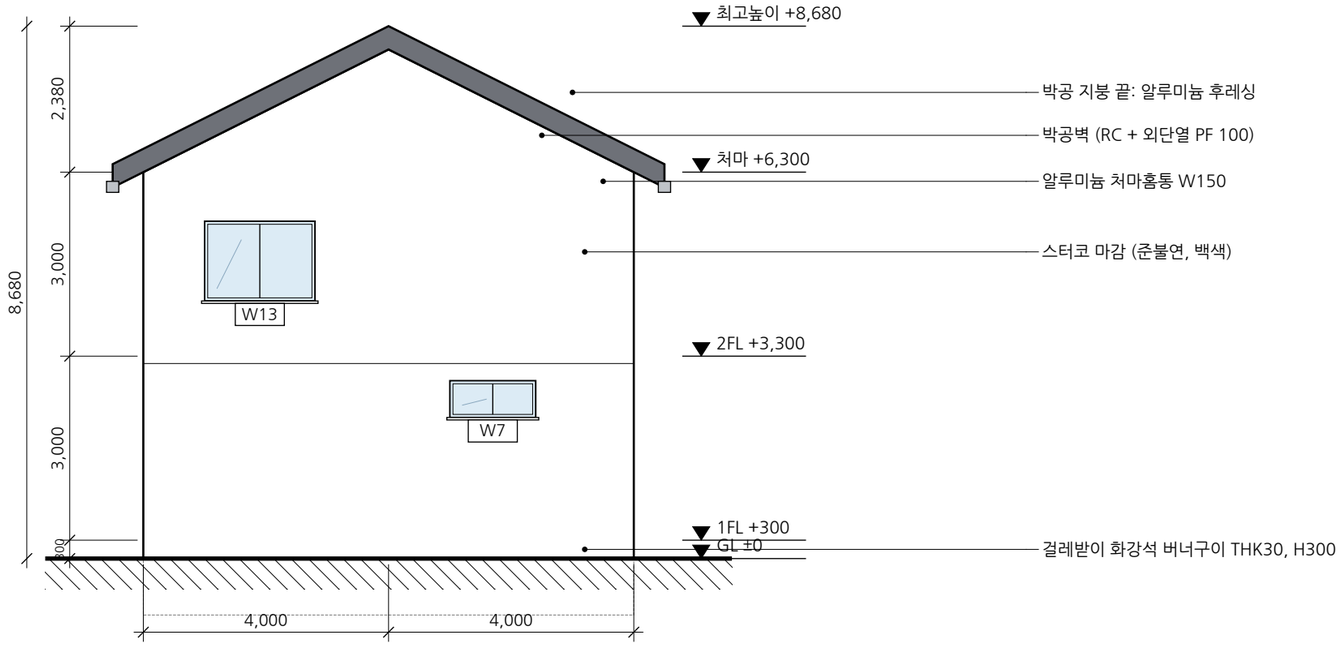

③ 동측 입면도

SCALE 1/100

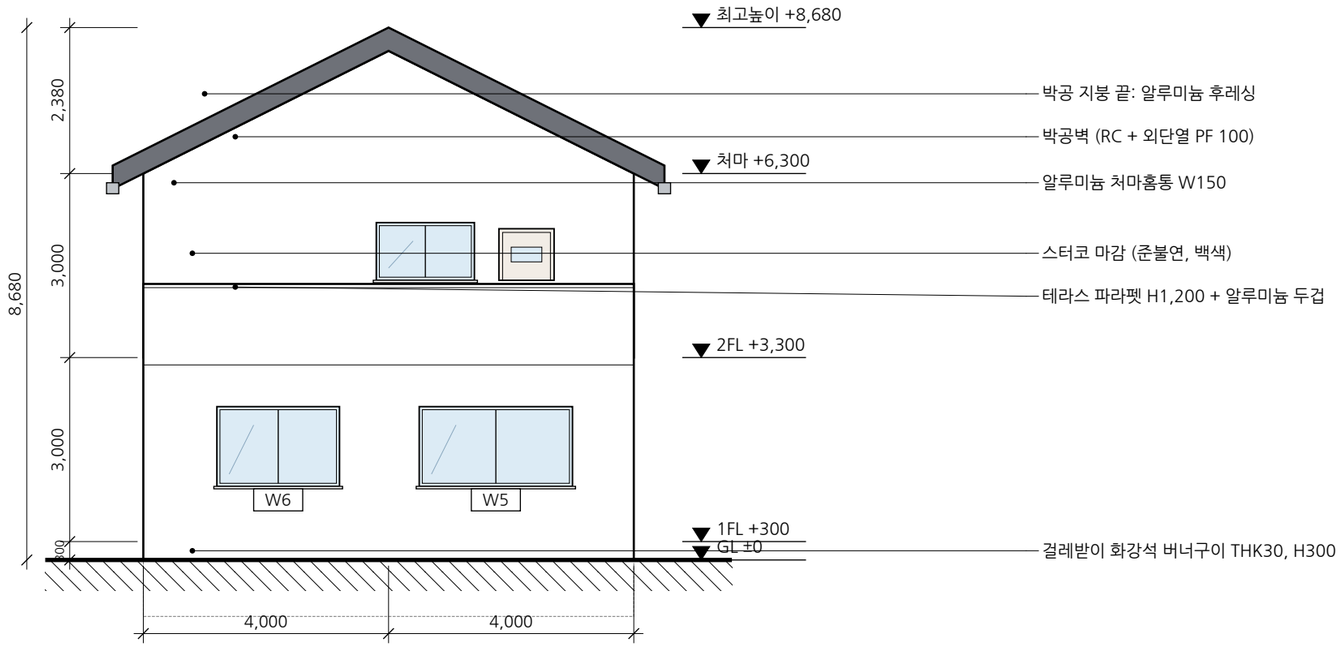

④ 서측 입면도

SCALE 1/100

PROJECT TITLE

경산 진량 단독주택 신축공사

PROJECT NO.

건축설계

NOTE

외부 마감

1. 외벽: 스터코(준불연) 백색, 걸레받이 화강석 THK30 H300
2. 지붕: 아스팔트 싱글 (흑회색), 처마 하부 알루미늄 소핏
3. 창호: PVC 시스템창호 (회색), 삼중 로이유리
4. 홈통: 알루미늄 처마홈통 W150, 선홈통 Ø100
5. 테라스 파라펫: RC + 외단열, 알루미늄 두겁

주의

인허가·실시설계 검토용 초안입니다.
건축사·구조기술사의 검토와 날인 전에는 시공·제출에 쓰지 않습니다.
치수 mm, 레벨 기준 GL±0 (설계 지반고).

NO.	DATE / DRAWN	REVISION NOTE
△		
△		
△		

경일대학교 건축학부
Kyungil University School of Architecture

ARCHITECT 건축사

APPROVED BY 승인

CHECKED BY 검토


DRAWN BY 도면작성: 연제욱 (20202672)

DATE 작성일자: 2026. 11.

DRAWING TITLE 도면작성: **동측 입면도 · 서측 입면도**

SCALE: 1/100

DRAWING NO.: **A-302**

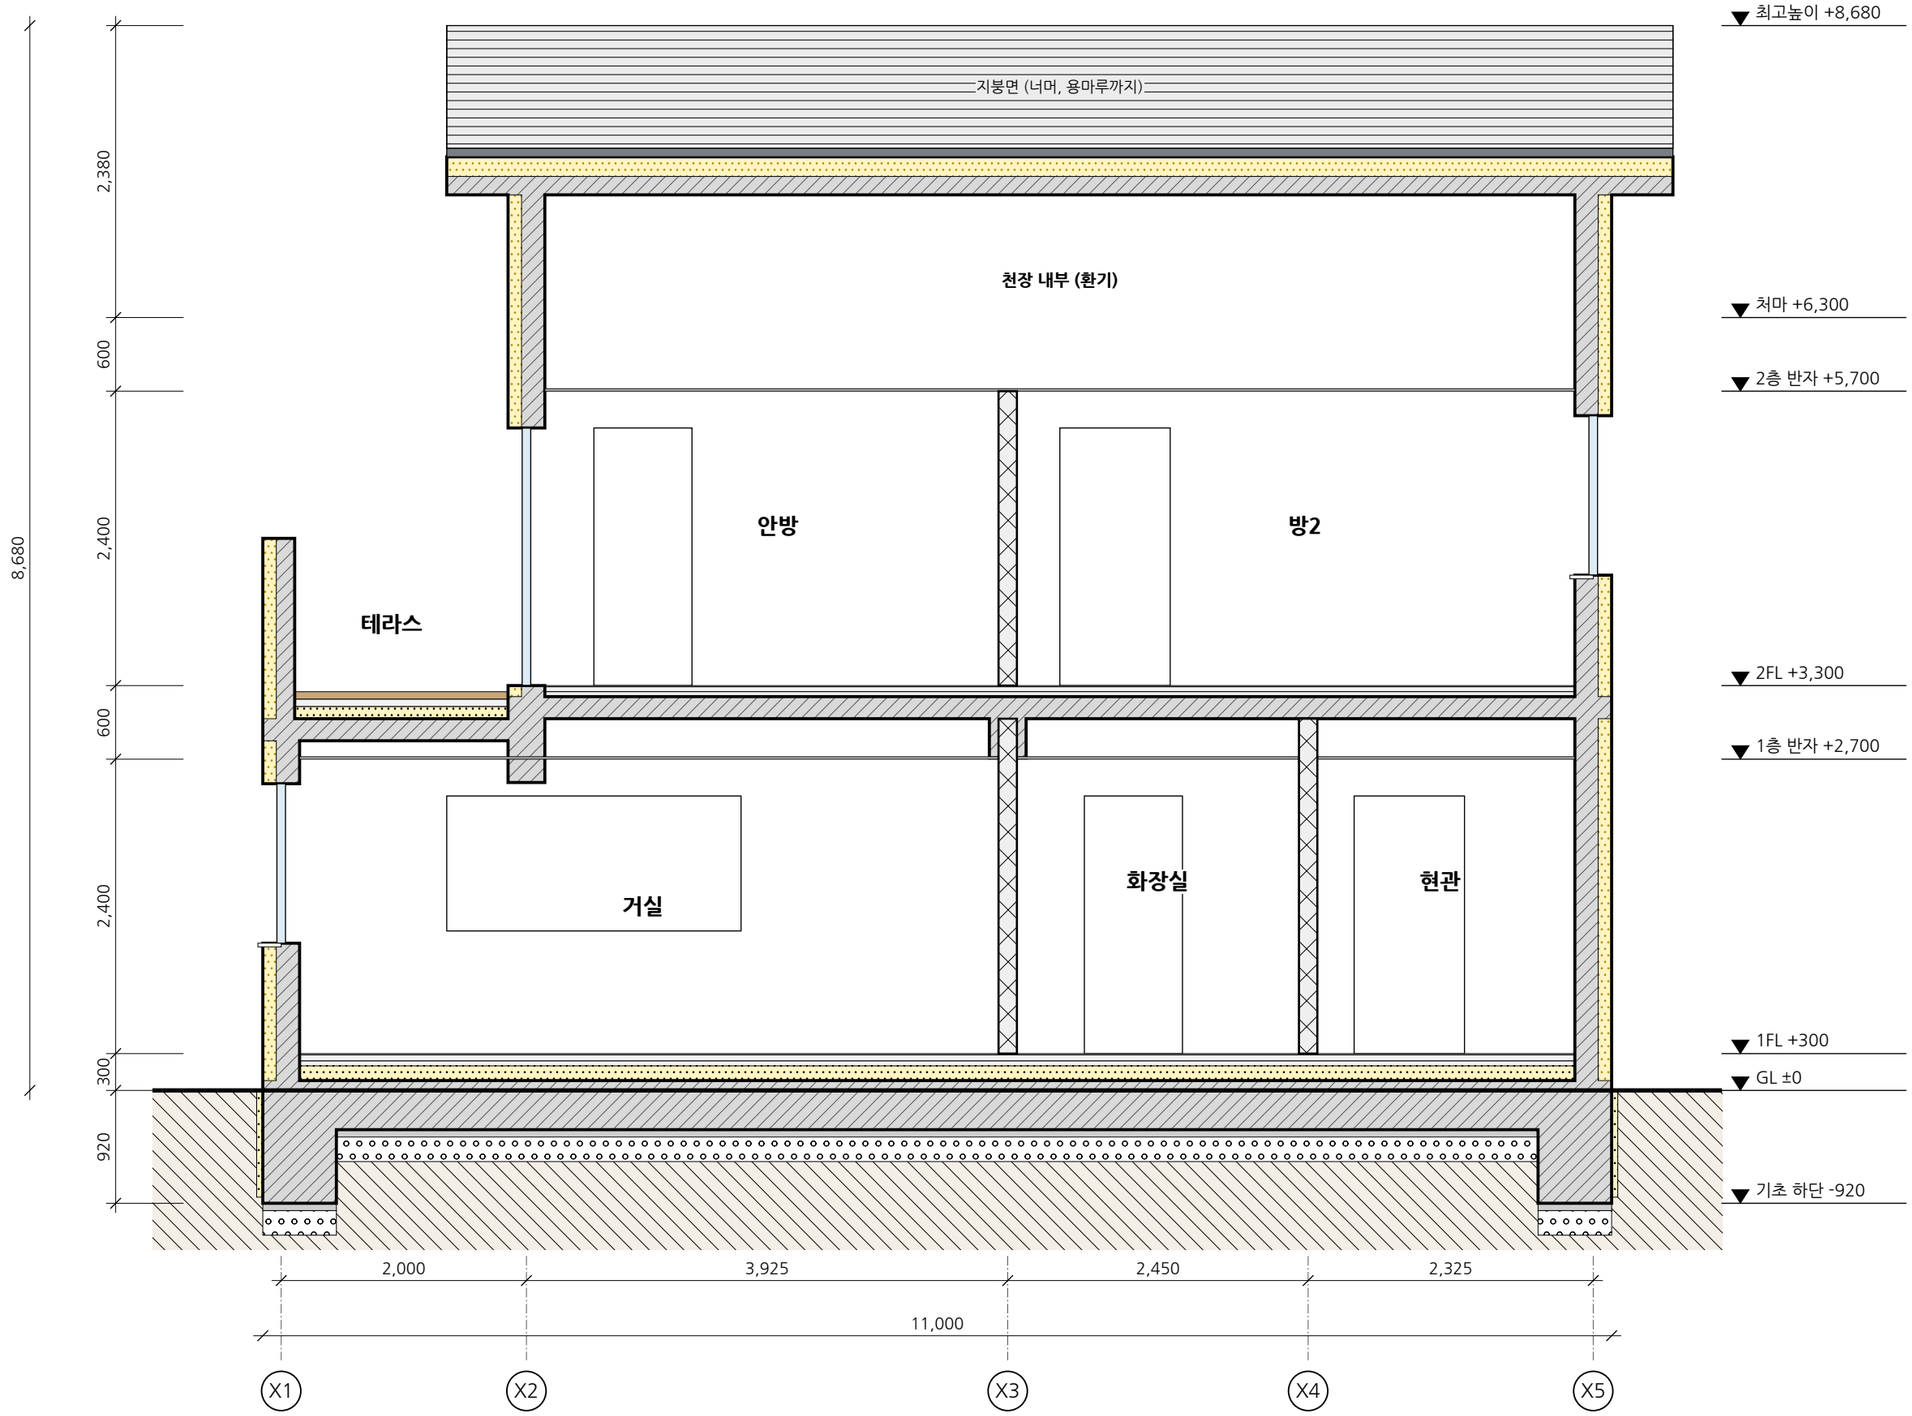

① 단면도 A-A'

SCALE 1/50

절단 위치: y = 11,000에서 북측을 봄

PROJECT TITLE

경산 진량 단독주택 신축공사

PROJECT NO.

건축설계

NOTE

부위별 구성

1. 지붕: 싱글 / 방수시트 / OSB 11 / 통기층 30 / PF보드 160 / RC 150
2. 외벽: 스터코 10 / PF보드 100 / RC 180 / 석고보드 9.5
3. 1층 바닥: 강마루 10 / 미장 50 / 기포 40 / XPS 특호 120 / PE필름 / 매트 400
4. 2층 바닥: 강마루 10 / 미장 40 / 기포 40 / RC 180
5. 테라스: 데크 / 보호몰탈 / 우레탄 도막방수 / PF보드 100 / RC 180
6. 기초: 매트 F1 THK400 + 외곽 기초보 FG1 (하단 GL-920)
7. 천장: 경량철골 천장틀 + 석고보드 9.5 2겹, 천장 내부 환기
8. 상세: A-501·A-502, 부재: S-001

주의

인허가·실시설계 검토용 초안입니다.
건축사·구조기술사의 검토와 날인 전에는 시공·제출에 쓰지 않습니다.
치수 mm, 레벨 기준 GL±0 (설계 지반고).

NO.	DATE	DRAWN	REVISION NOTE
△			
△			
△			

경일대학교
건축학부
Kyungil University
School of Architecture

ARCHITECT 건축사

APPROVED BY 승인

CHECKED BY 검토


DRAWN BY 도면작성: 연제욱 (20202672)

DATE 작성일자: 2026. 11.

DRAWING TITLE 도면작성: **단면도 A-A'**

SCALE: 1/50

DRAWING NO.: **A-401**

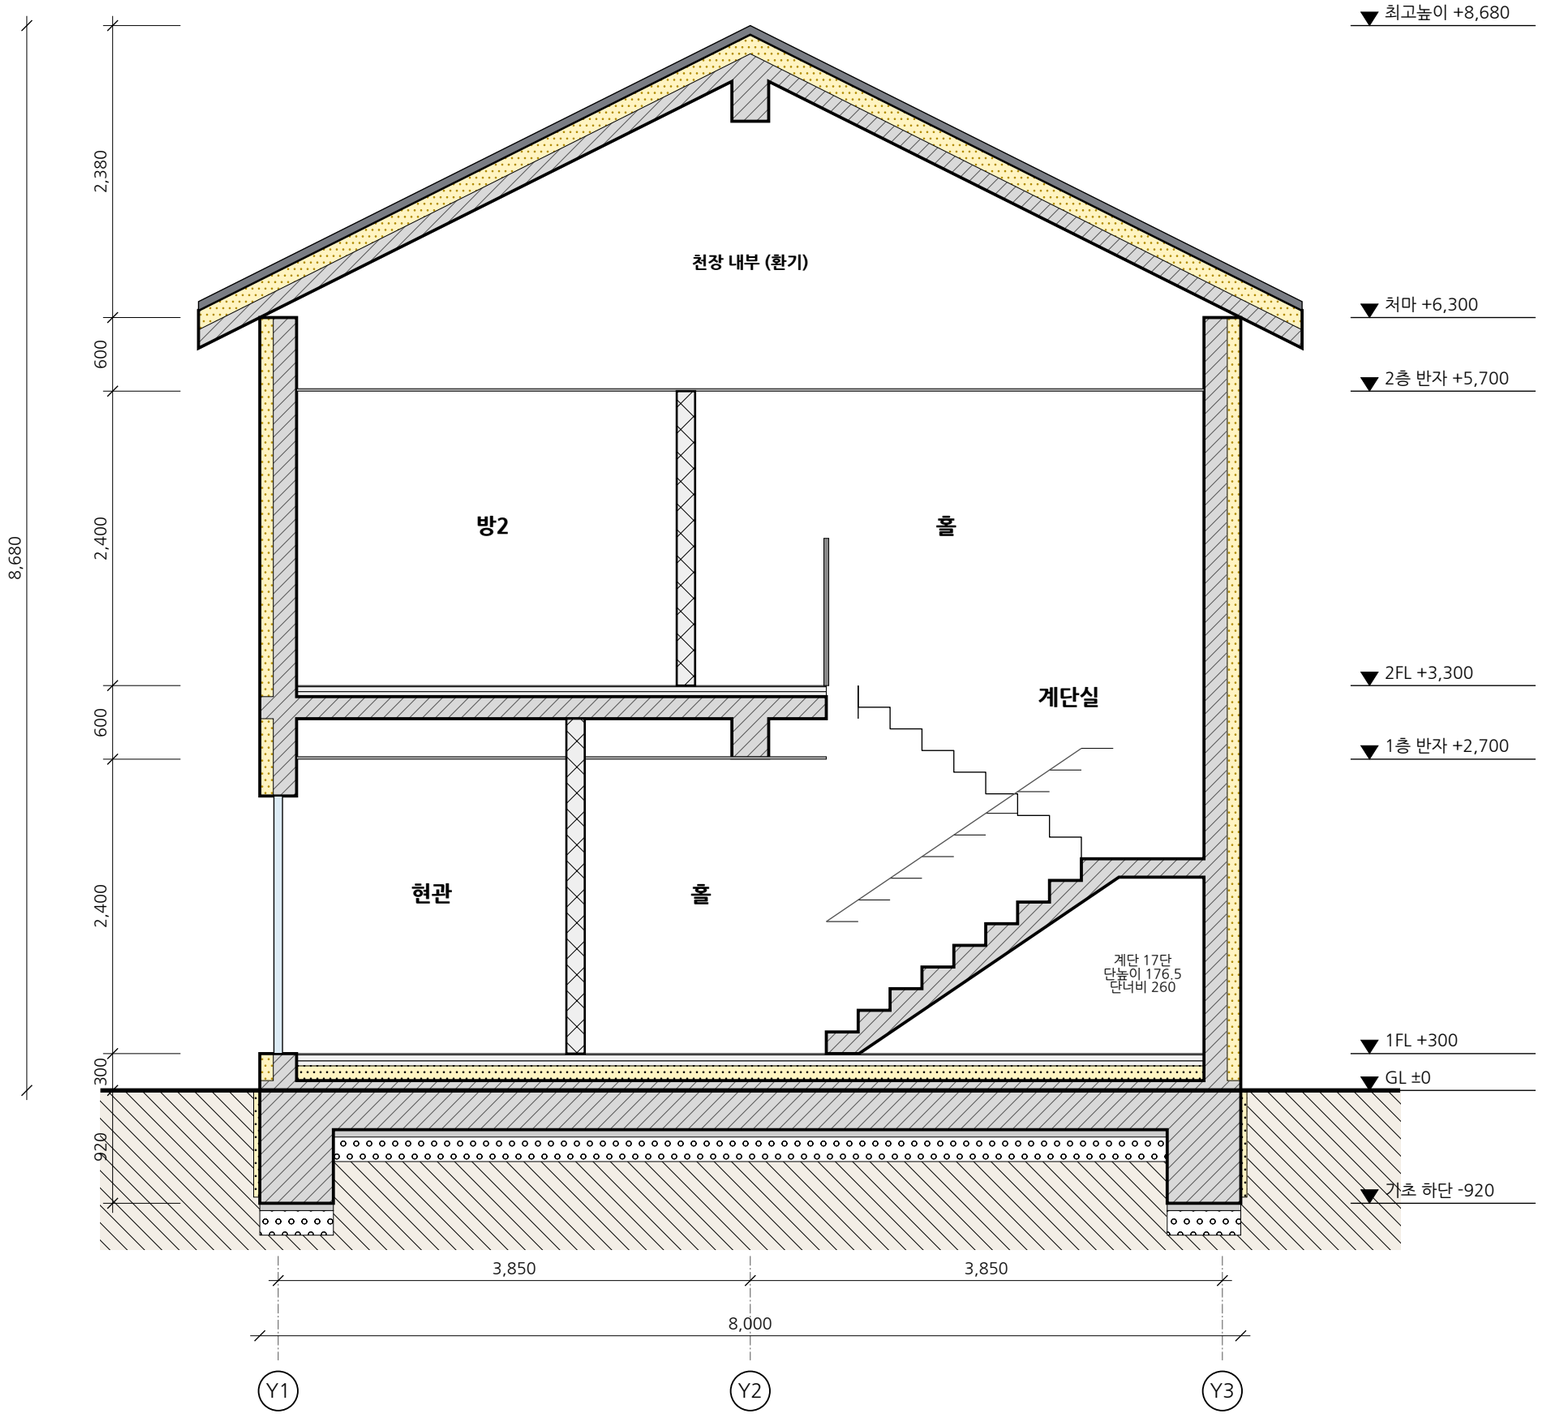

1 단면도 B-B'

SCALE 1/50

절단 위치: x = 11,650에서 서측을 봄 (계단 절단)

PROJECT TITLE

경산 진량 단독주택 신축공사

PROJECT NO.

건축설계

NOTE

부위별 구성

1. 지붕: 싱글 / 방수시트 / OSB 11 / 통기층 30 / PF보드 160 / RC 150
2. 외벽: 스터코 10 / PF보드 100 / RC 180 / 석고보드 9.5
3. 1층 바닥: 강마루 10 / 미장 50 / 기포 40 / XPS 특호 120 / PE필름 / 매트 400
4. 2층 바닥: 강마루 10 / 미장 40 / 기포 40 / RC 180
5. 테라스: 데크 / 보호몰탈 / 우레탄 도막방수 / PF보드 100 / RC 180
6. 기초: 매트 F1 THK400 + 외곽 기초보 FG1 (하단 GL-920)
7. 천장: 경량철골 천장틀 + 석고보드 9.5 2겹, 천장 내부 환기
8. 상세: A-501·A-502, 부재: S-001

주의
인허가·실시설계 검토용 초안입니다.
건축사·구조기술사의 검토와 날인 전에는 시공·제출에 쓰지 않습니다.
치수 mm, 레벨 기준 GL±0 (설계 지반고).

NO.	DATE / DRAWN	REVISION NOTE
△		
△		
△		

경일대학교
건축학부
Kyungil University
School of Architecture

ARCHITECT 건축사

APPROVED BY 승인

CHECKED BY 검토


DRAWN BY 도면작성: 연제욱 (20202672)

DATE 작성일자: 2026. 11.

DRAWING TITLE 도면작성: **단면도 B-B'**


SCALE: 1/50

DRAWING NO.: **A-402**

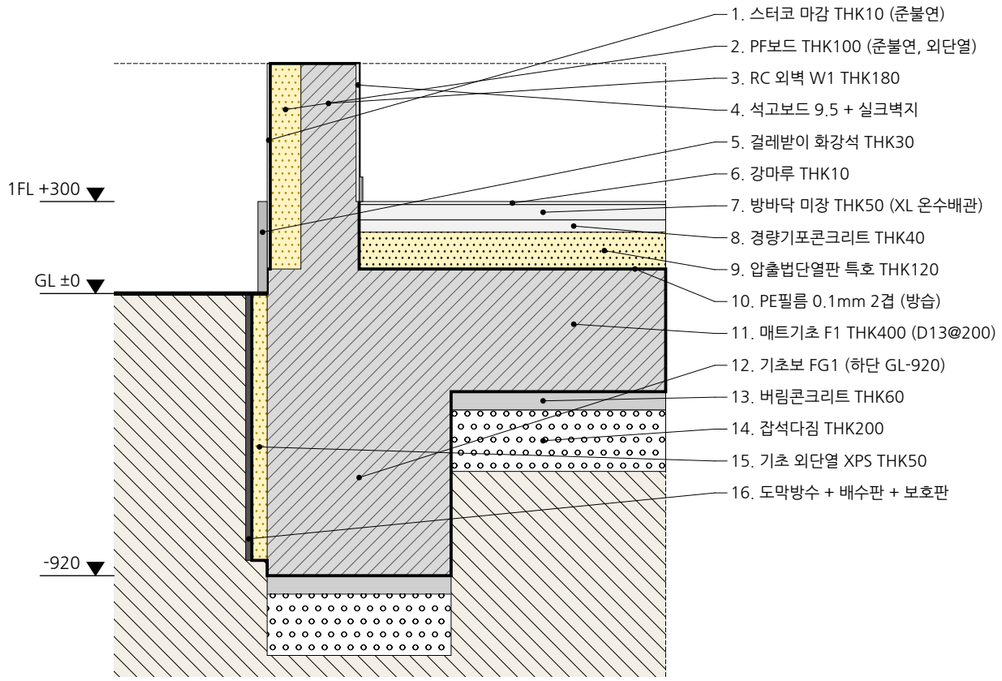

① 상세 1 기초·외벽·1층 바닥

SCALE 1/20

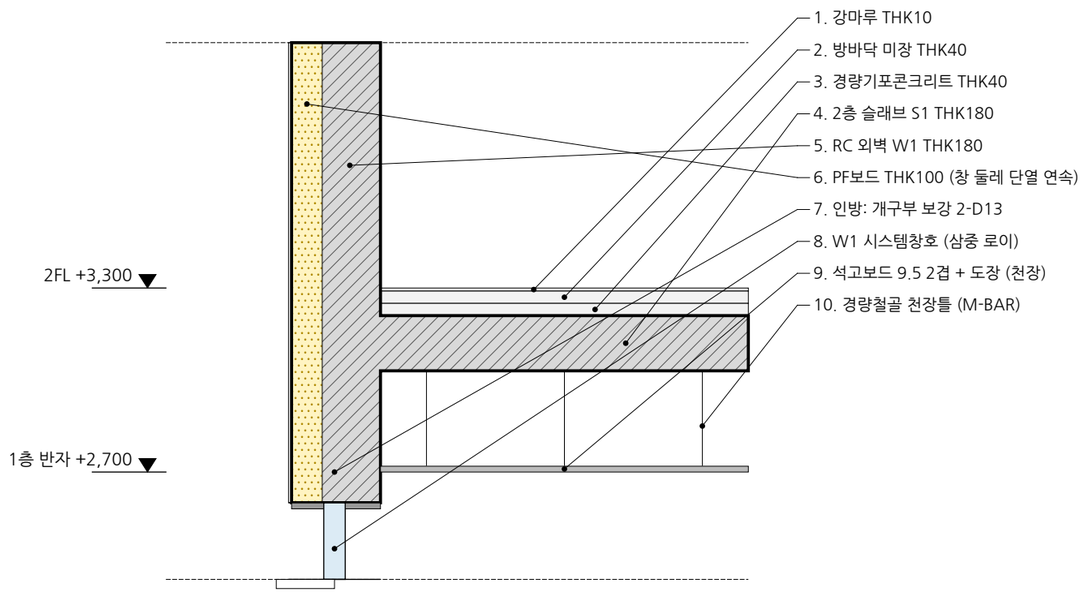

② 상세 2 2층 바닥·외벽

SCALE 1/20

PROJECT TITLE

경산 진량 단독주택 신축공사

PROJECT NO.

건축설계

NOTE

단열·방수
외벽 PF보드(준불연) 100 외단열, 기초 외단열 XPS 50 + 도막방수 + 배수판.
창 둘레 단열재는 끊기지 않게 프레임까지 붙입니다.

철근
부재 배근은 S-001 부재일람표 (예비 산정).

주의
인허가·실시설계 검토용 초안입니다.
건축사·구조기술사의 검토와 날인 전에는 시공·제출에 쓰지 않습니다.
치수 mm, 레벨 기준 GL±0 (설계 지반고).

NO.	DATE / DRAWN	REVISION NOTE
△		
△		
△		

경일대학교
건축학부
Kyungil University
School of Architecture

ARCHITECT 건축사

APPROVED BY 승인

CHECKED BY 검토


DRAWN BY 도면작성: 연제욱 (20202672)

DATE 작성일자: 2026. 11.

DRAWING TITLE 도면작성: **상세 (기초·2층 바닥)**


SCALE: 1/20

DRAWING NO.: **A-501**

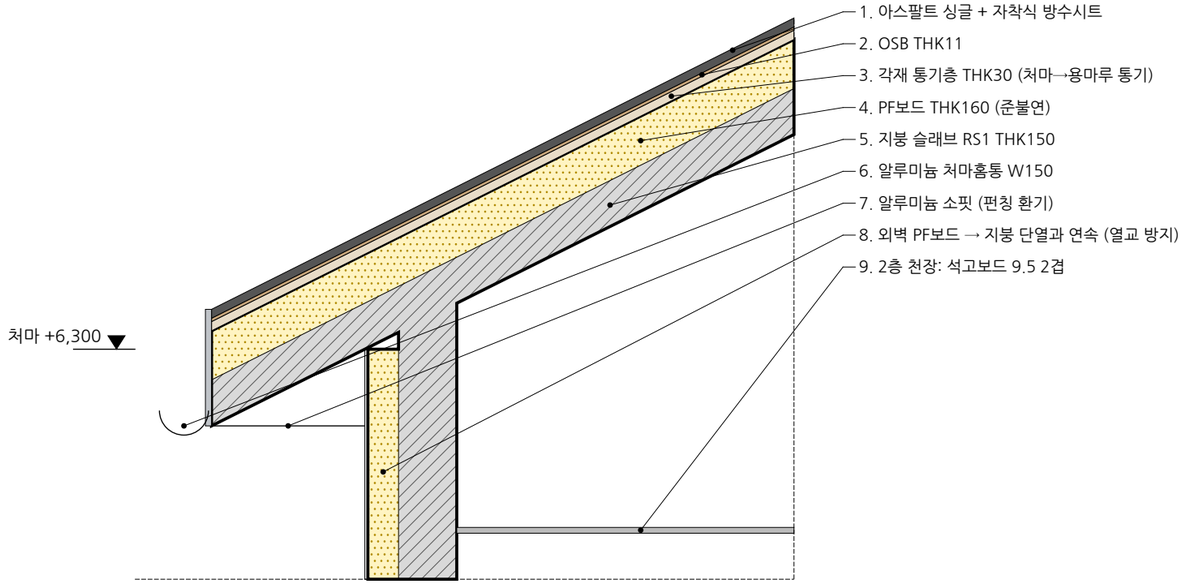

③ 상세 3 처마

SCALE 1/20

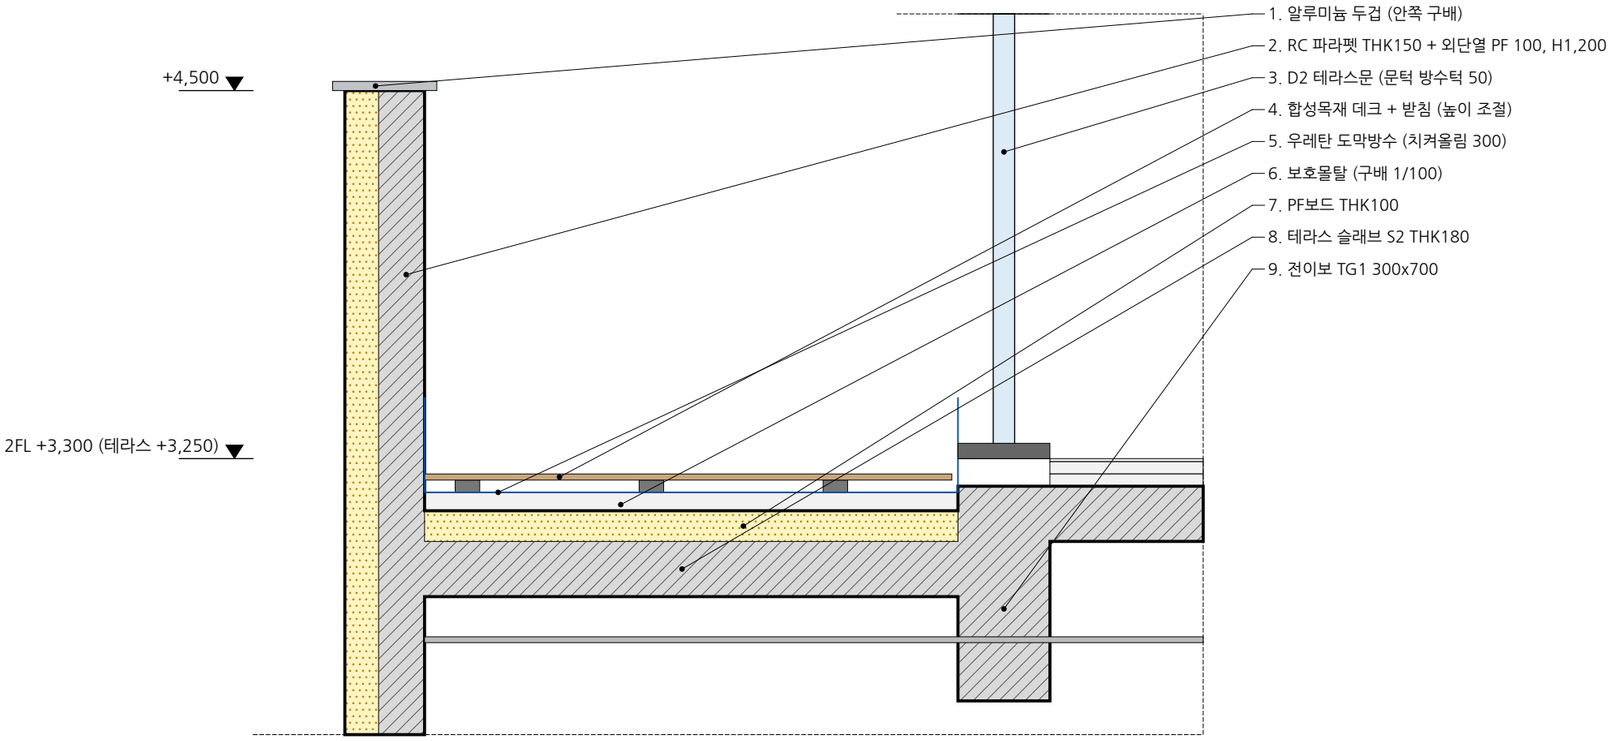

④ 상세 4 테라스·파라펫

SCALE 1/20

PROJECT TITLE

경산 진량 단독주택 신축공사

PROJECT NO.

건축설계

NOTE

통기·방수
처마 소핏에서 용마루 벤트까지 통기층 30 연속.
테라스 우레탄 도막방수는 파라펫·벽에 300 치켜올림, 문턱 방수턱 50.

열교
외벽 단열과 지붕 단열을 처마에서 연속시킵니다.

주의
인허가·실시설계 검토용 초안입니다.
건축사·구조기술사의 검토와 날인 전에는 시공·제출에 쓰지 않습니다.
치수 mm, 레벨 기준 GL±0 (설계 지반고).

NO.	DATE	REVISION NOTE
	DRAWN	

경일대학교
건축학부
Kyungil University
School of Architecture

ARCHITECT 건축사

APPROVED BY 승인

CHECKED BY 검토

DRAWN BY 도면작성: 연제욱 (20202672)

DATE 작성일자: 2026. 11.

DRAWING TITLE 도면작성

상세 (처마·테라스)

SCALE: 1/20

DRAWING NO.: **A-502**

구조 일반사항

1. 설계기준: 건축구조기준 (KDS 41), 콘크리트구조 설계기준 (KDS 14 20)
2. 재료: 콘크리트 fck = 24 MPa, 철근 SD400 (D10~D22), 이음·정착은 KDS 14 20 52
3. 하중: 고정하중은 실제 구성으로 산정, 활하중 주거 2.0 kN/㎡, 지붕 1.0 kN/㎡
4. 적설·풍하중: 경산시 지역 기준값 (KDS 41 12 00) — 구조계산서에서 확정
5. 내진: 2층 이상 → 구조안전 확인 대상 (건축법 시행령 제32조), 내진등급 II
6. 지반: 허용지내력 fe ≥ 150 kN/㎡ 가정 — 지반조사(평판재하시험) 후 확정
7. 피복두께: 흙에 접하는 기초 75, 흙에 접하는 벽 50, 실내 슬래브·벽 20, 보 40
8. 개구부 보강: 개구부 둘레 2-D13, 모서리 사선보강 2-D13 (L=1,000)
9. 부재 크기·배근은 예비 산정값이며 구조계산서와 구조기술사 검토로 확정한다.

부재일람표

부호	부재	크기	배근	비고
F1	매트기초	THK400	상·하단 D13@200 양방향	피복 상 50 / 하 75
FG1	외곽 기초보	600 x 1,000 (매트 포함)	상 4-D19, 하 4-D19, 늑근 D10@200	동결심도 이하 GL-920
W1	외벽 (내력벽)	THK180	수직 D10@200, 수평 D10@250 복배근	개구부 보강 2-D13
S1	2층 바닥 슬래브	THK180	단변 D10@200, 장변 D10@250 상·하단	2방향 슬래브
S2	테라스 슬래브	THK180 (FL-450)	단변 D10@200, 장변 D10@250 상·하단	단차 지지
RS1	지붕 슬래브	THK150 (경사 5/10)	D10@200 양방향 상·하단	처마 캔틸레버 500
G1	큰보 (Y2열)	300 x 500	상 3-D19, 하 4-D19, 늑근 D10@150	연속보
B1	작은보 (X3열)	300 x 500	상 3-D16, 하 3-D19, 늑근 D10@150	G1 교차
TG1	전이보 (X2열)	300 x 700	상 4-D22, 하 5-D22, 늑근 D10@150	2층 외벽 지지
RB1	용마루보	300 x 400	상 3-D16, 하 3-D16, 늑근 D10@200	박공벽 지지

하중표 (kN/㎡, 추정)

부위	고정	활
지붕 (경사)	5.4	1.0
2층 바닥	6.2	2.0
테라스	7.0	3.0
계단	6.5	3.0

PROJECT TITLE

경산 진량 단독주택 신축공사

PROJECT NO. 건축설계

NOTE

구조 형식
철근콘크리트 벽식구조 + 보 (G1, B1, TG1, RB1), 매트기초.

확정 필요
구조계산서, 지반조사, 지역 적설·풍하중.

주의
인허가·실시설계 검토용 초안입니다.
건축사·구조기술사의 검토와 날인 전에는 시공·제출에 쓰지 않습니다.
치수 mm, 레벨 기준 GL±0 (설계 지반고).

NO.	DATE	REVISION NOTE
△		
△		
△		

경일대학교 건축학부
Kyungil University School of Architecture

ARCHITECT 건축사

APPROVED BY 승인

CHECKED BY 검토

DRAWN BY 도면작성 연제욱 (20202672)


DATE 작성일자 2026. 11.

DRAWING TITLE 도면작성

구조 일반사항·부재일람표


SCALE NONE

DRAWING NO. **S-001**

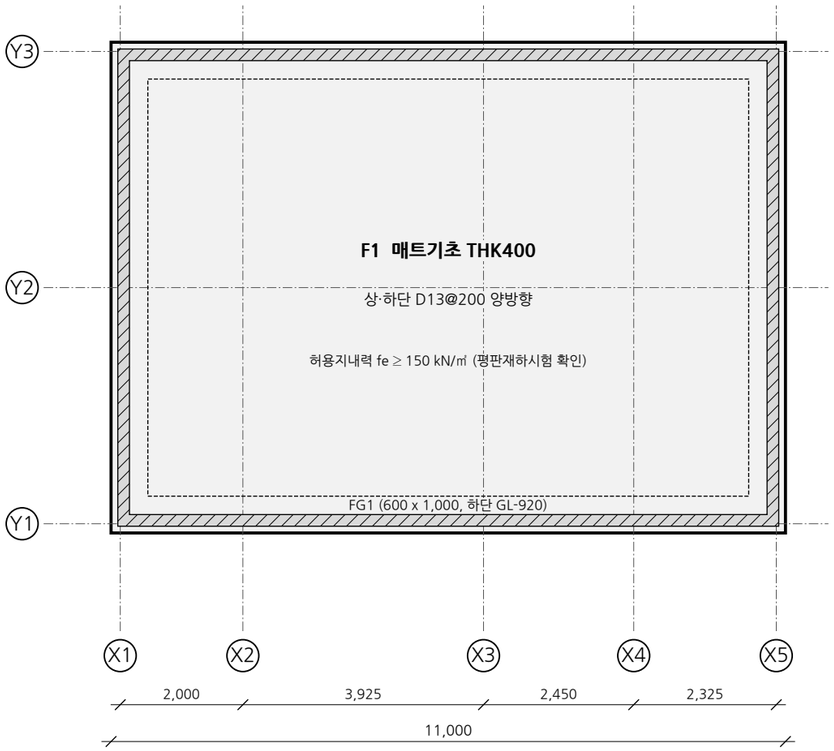


① 기초 구조평면도

SCALE 1/100

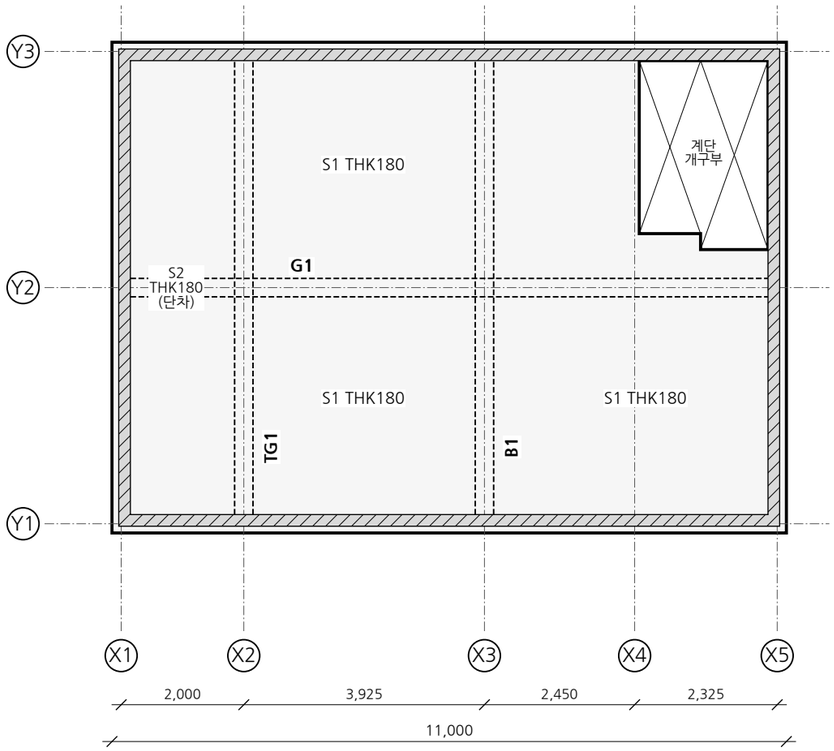

② 2층 바닥 구조평면도

SCALE 1/100

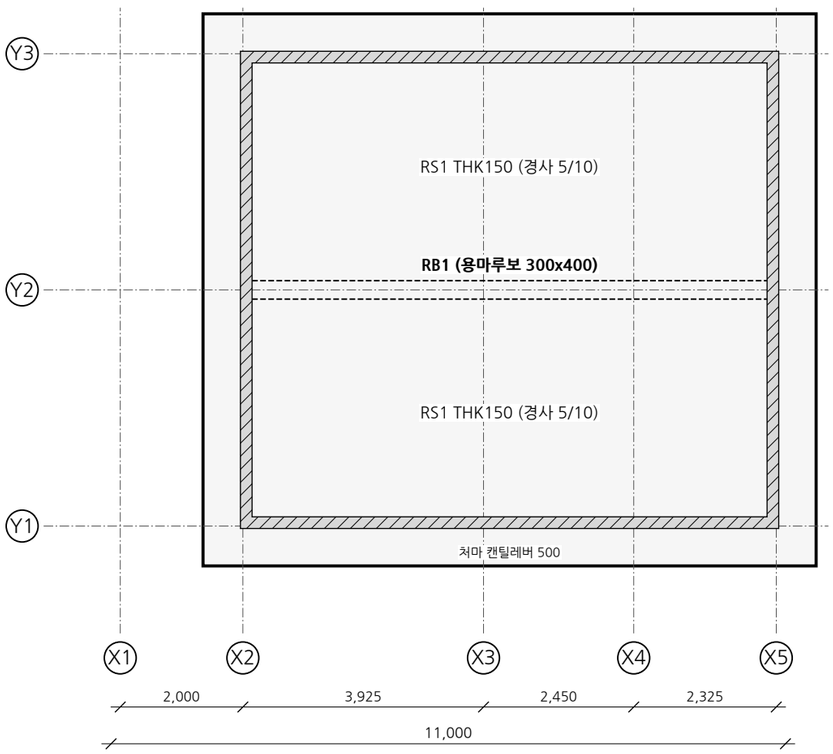

③ 지붕 구조평면도

SCALE 1/100

범례

W1 RC 내력벽 THK180 (해당 층 아래 벽)

보 (슬래브 아래)

PROJECT TITLE

경산 진량 단독주택 신축공사

PROJECT NO.

건축설계

NOTE

보

TG1: 2층 서측 외벽(X2열)이 1층 거실 위에 놓이므로 전이보로 받친다.

G1·B1: 2층 바닥 슬래브 경간을 5.7 m 이하로 나눈다.

RB1: 동·서 박공벽에 걸친 용마루보.

계단

RC 계단 (경사판 THK150), 1층 바닥·참·2층 슬래브에 정착.

주의

인허가·실시설계 검토용 초안입니다.
건축사·구조기술사의 검토와 날인 전에는 시공·제출에 쓰지 않습니다.
치수 mm, 레벨 기준 GL±0 (설계 지반고).

NO.	DATE / DRAWN	REVISION NOTE
△		
△		
△		

경일대학교
건축학부
Kyungil University
School of Architecture

ARCHITECT 건축사

APPROVED BY 승인

CHECKED BY 검토

DRAWN BY 도면작성: 연제욱 (20202672)

DATE 작성일자: 2026. 11.

DRAWING TITLE 도면작성

구조 평면도

SCALE: 1/100

DRAWING NO.: **S-101**